

49000 ANGERS

1 Avenue du Bois l'Abbé
49070 BEAUCOUZÉ
Tél: 02 41 36 88 50



CHEVALLIER
CONSTRUCTION


Pht Rez De Chaussée - Coffrage & Armatures -

Repérage de Zone :

Date	Modifications						Ind	Echelles	
06/12/20	1ère DIFFUSION						A	Plans :	-
19/01/21	Suppression des sommiers B.A, remplacés par chaînages linéaires existant.						B	Coupes :	1/10
-	-						C	Détails :	-
-	-						D		
-	-						E		
-	-						F		
Dessiné par : P. MALEVRE Ligne directe : 07.83.869.820 Ingénieur: RIVRON Fabien		N° AFF	PHASE	ZONE	TYPE	NIV	NUM	INDICE	
		P201101	EXE	A	CFA	RC	001	B	


RDC

0

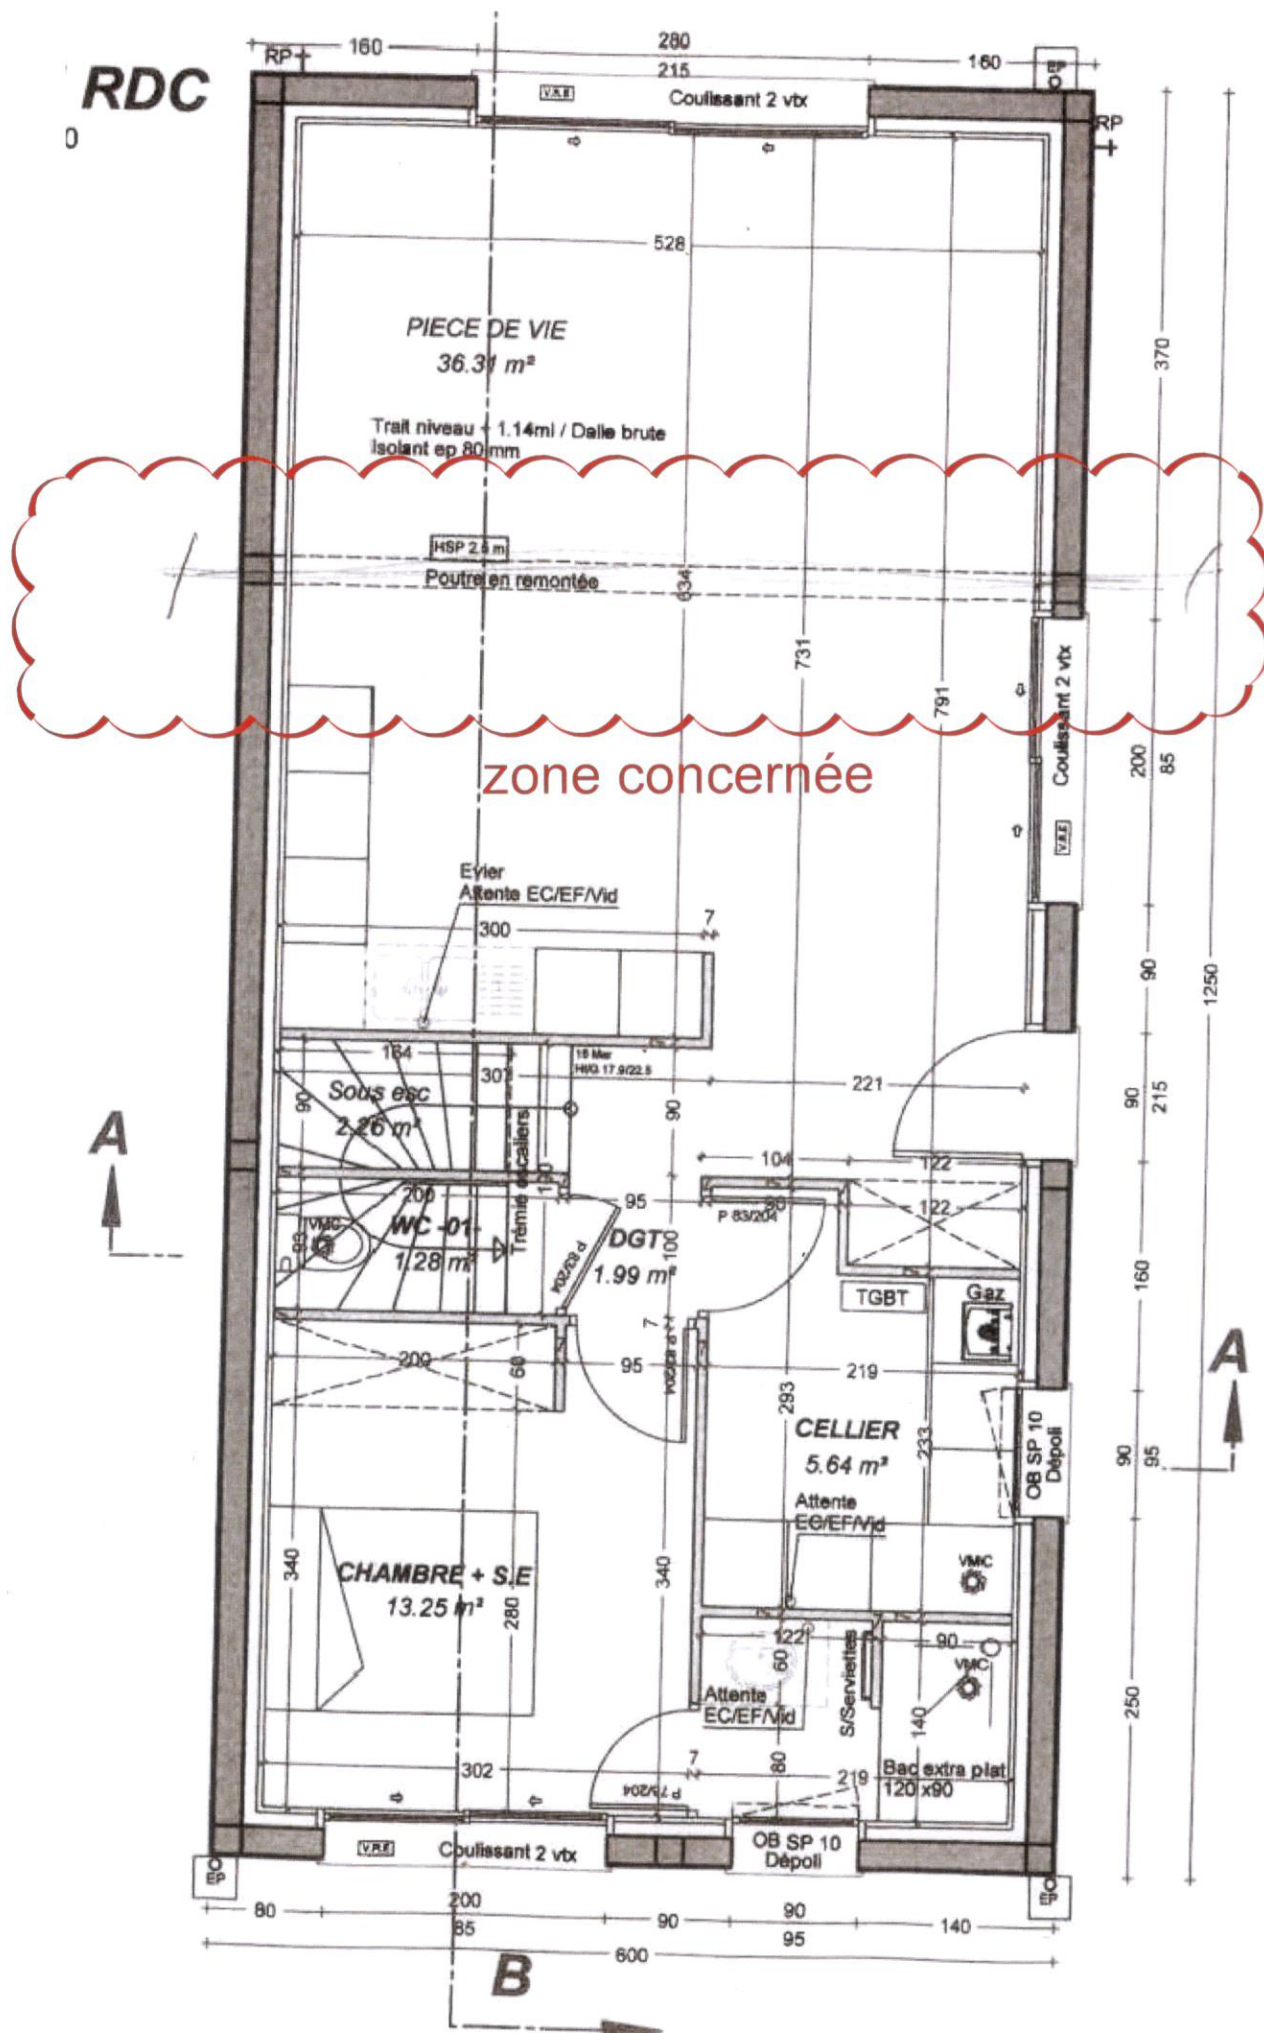


VUE EN PLAN ARCHITECTE

VUES EN PLAN

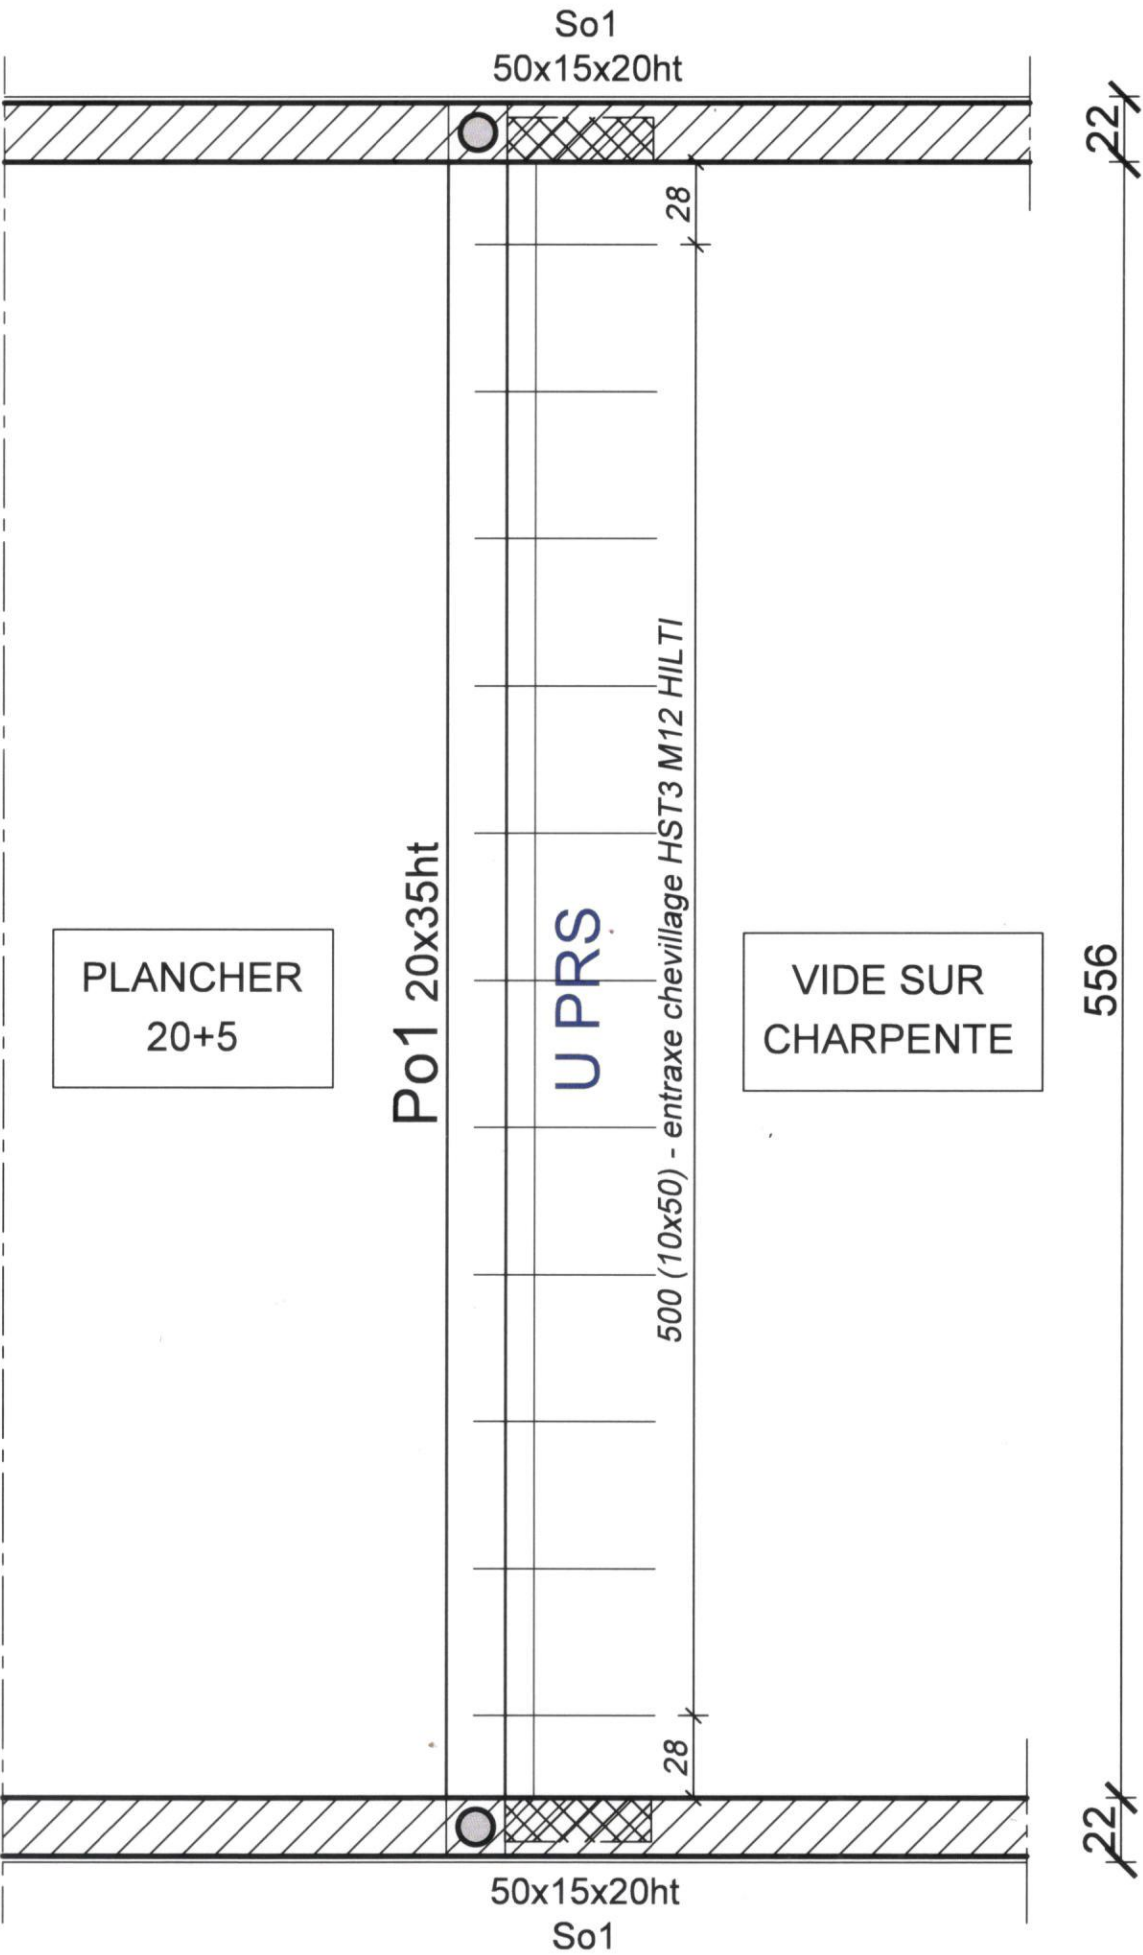


COUPE / RENFORCEMENT

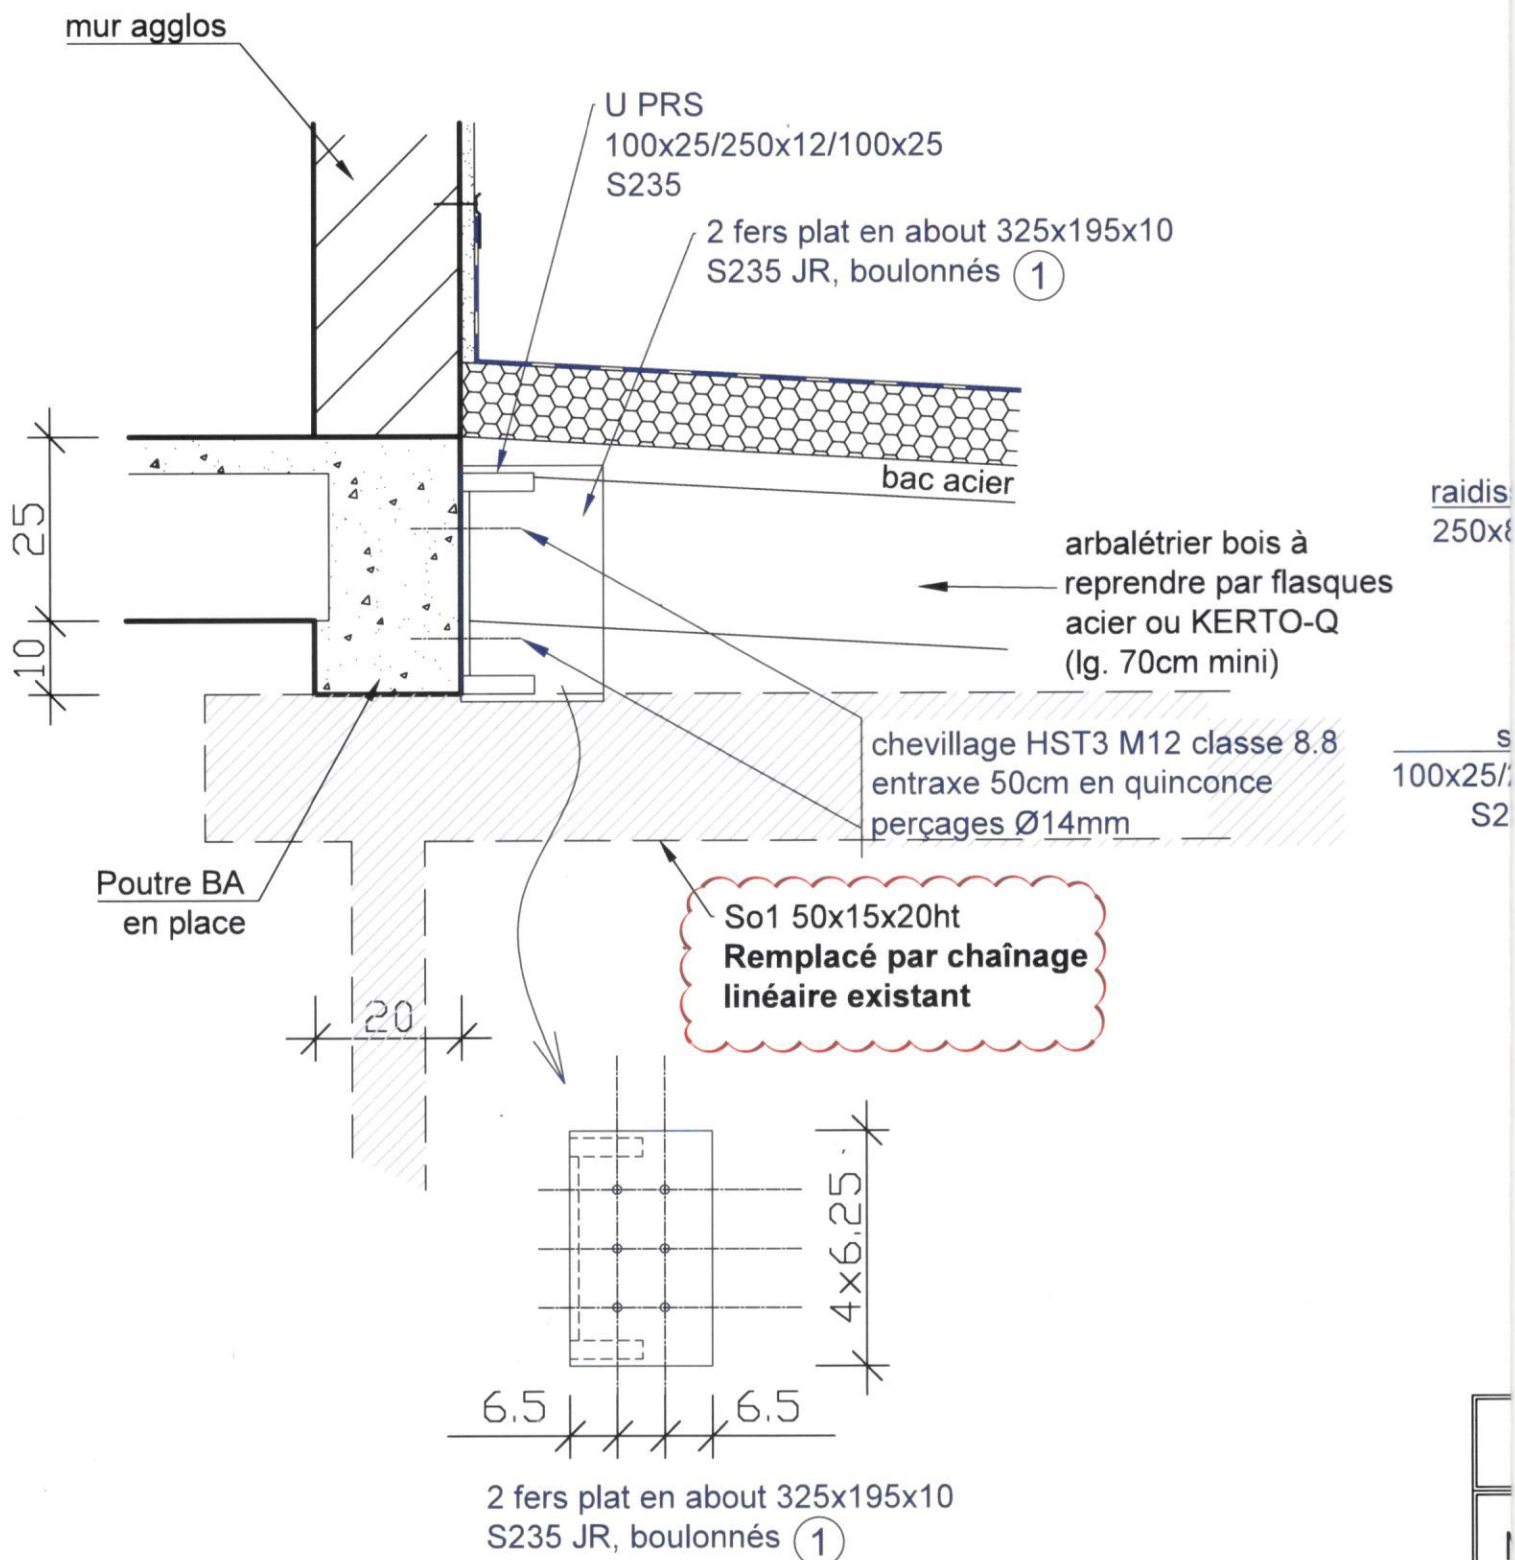

**Cordons de soudures
gorges à 5mm**

COUPE / APPUIS (x2)

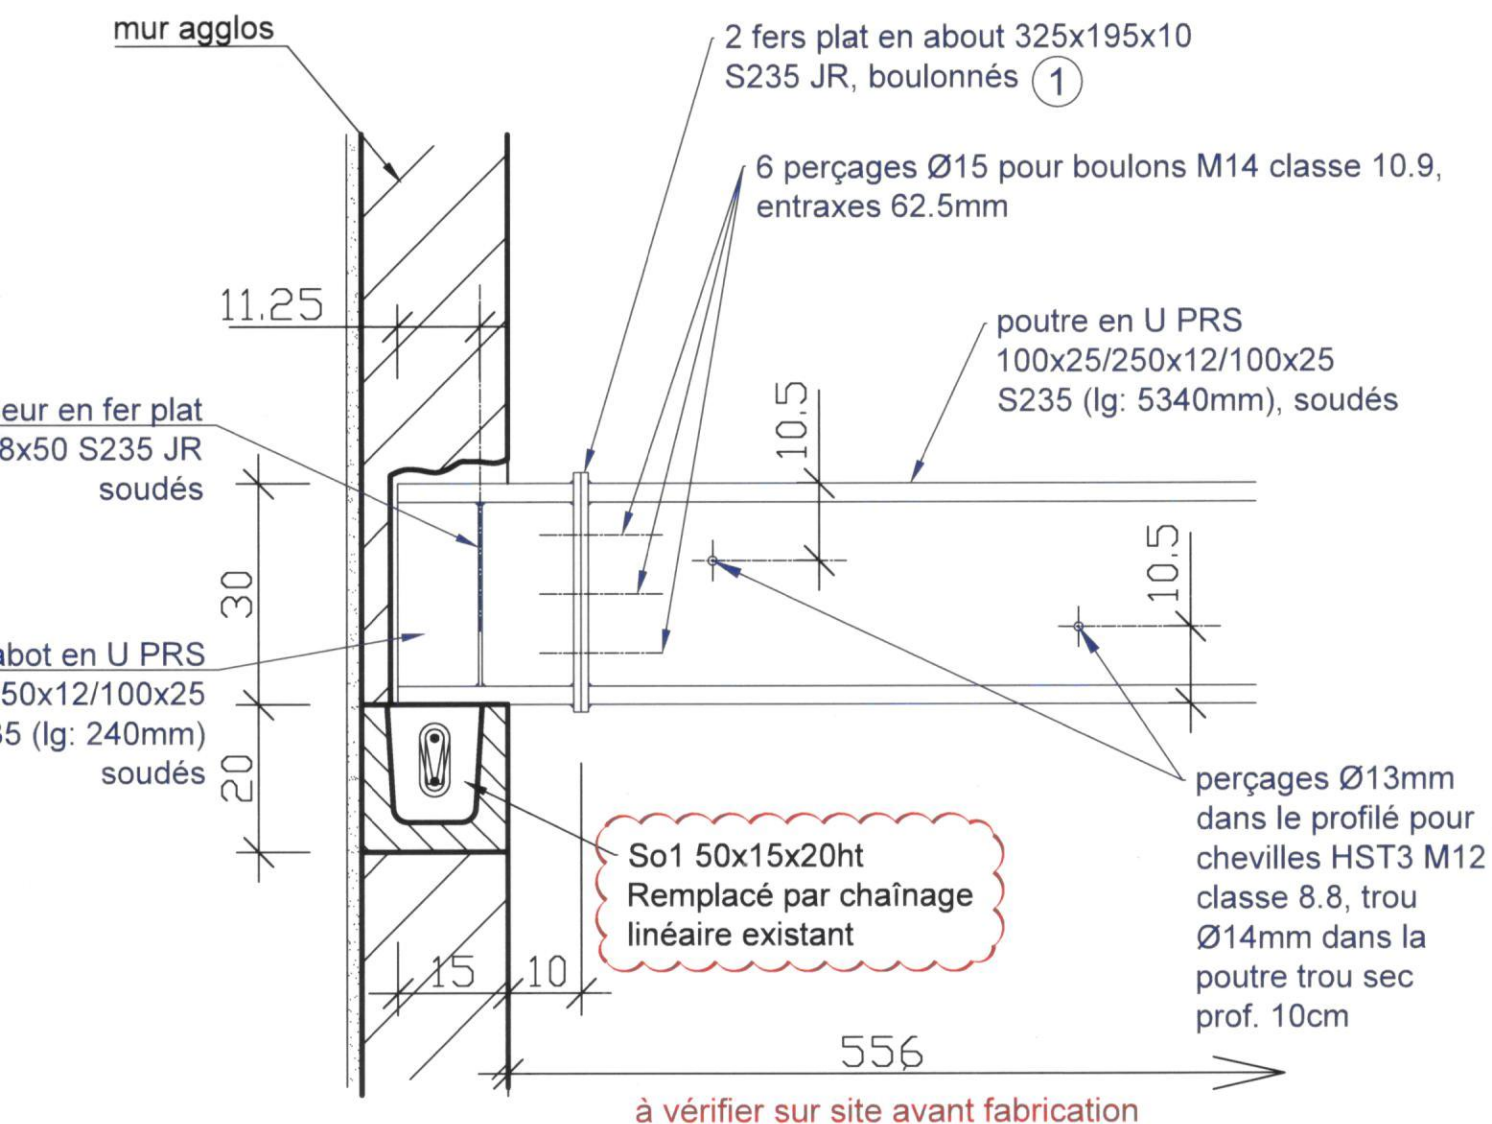


Nomenclature générale des aciers .

°	TYPE	Ø	Nombre			Esp	Long. Unitaire	Façonnage	Mandrin (cm) 	Long. TOTALE	Indice
			Par Elément	d'éléments	Total						
1	HA	10	1	2	2		44	<u>44</u>		88	
2	HA	6	5	2	10	10	0				


: LONGUEUR MOYENNE

Diamètre moyen : 10.0


1 élément (épaisseur 12mm)

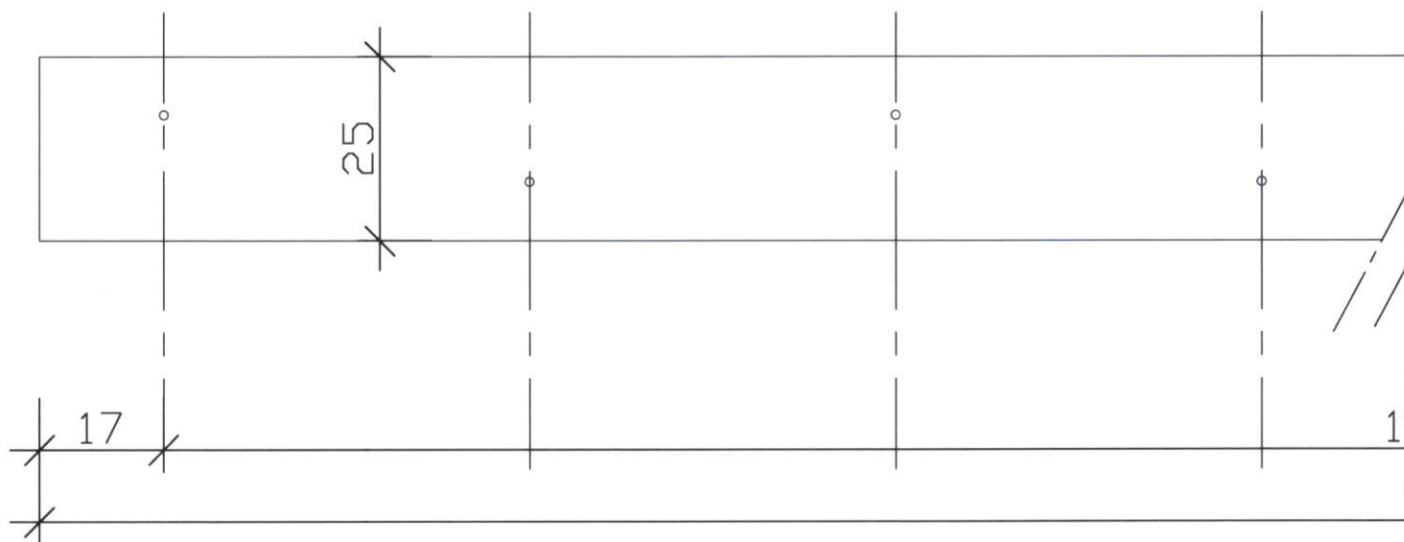


2 éléments (épaisseur 25mm)

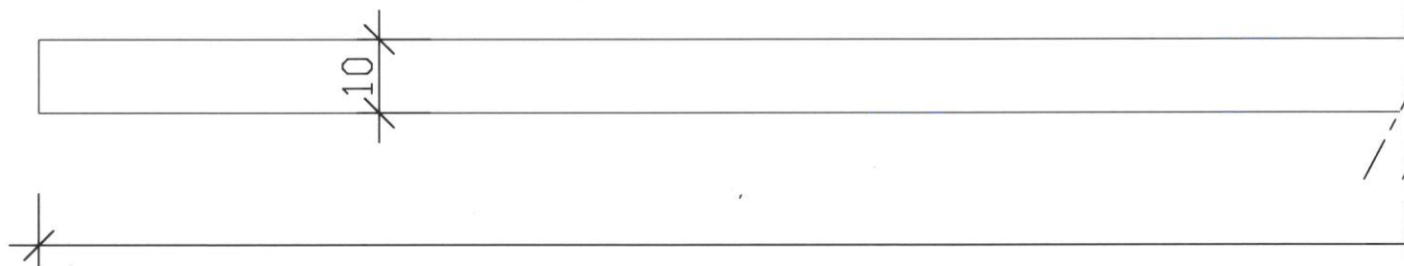



2 éléments (épaisseur 12mm)

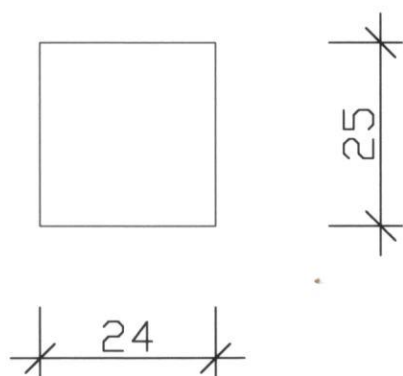

4 éléments (épaisseur 25mm)


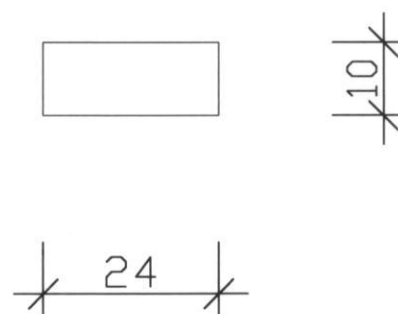


DETAILS

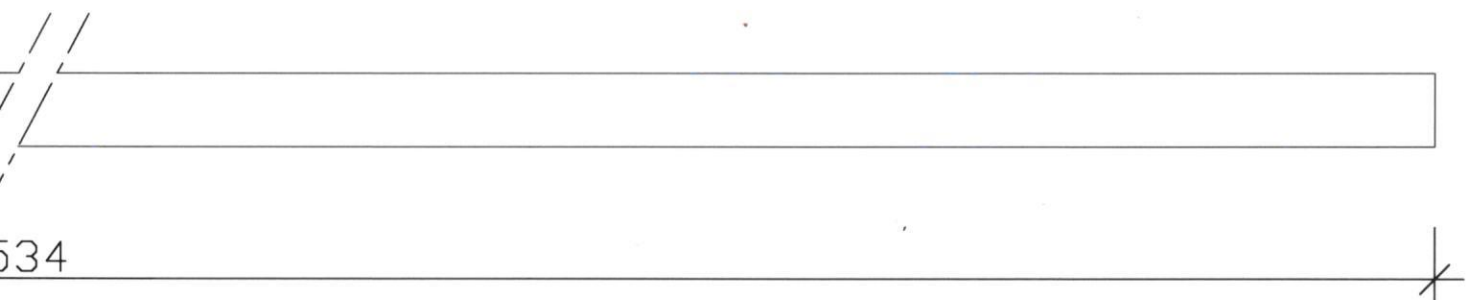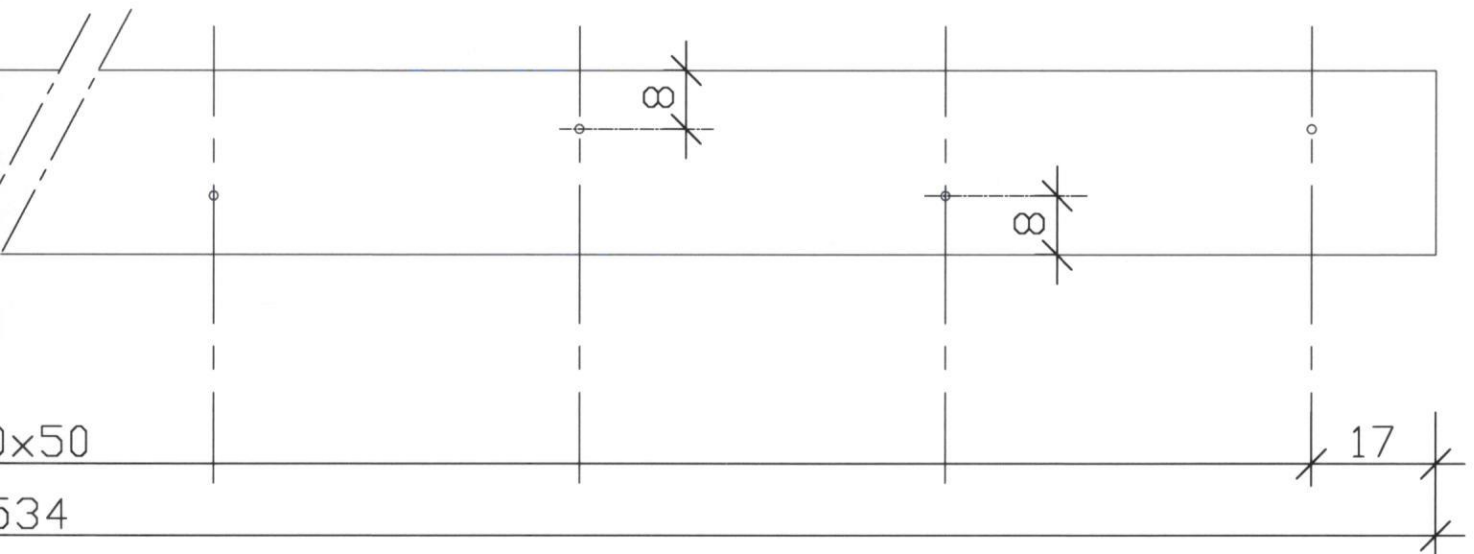

2 éléments (épaisseur 5mm)

2 éléments (épaisseur 10mm)

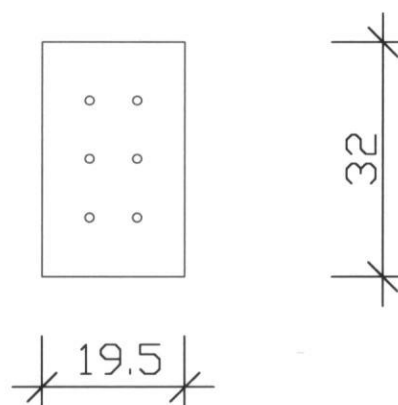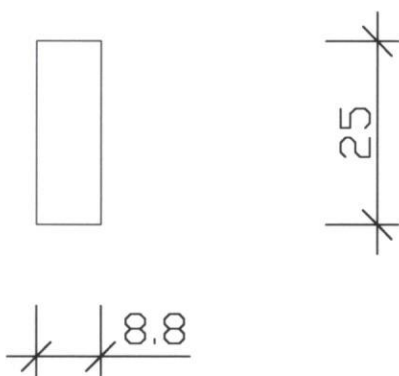

Chargé d'affaire : Malèvre Patrick

[illegible]