



Plan de Voirie et des Réseaux

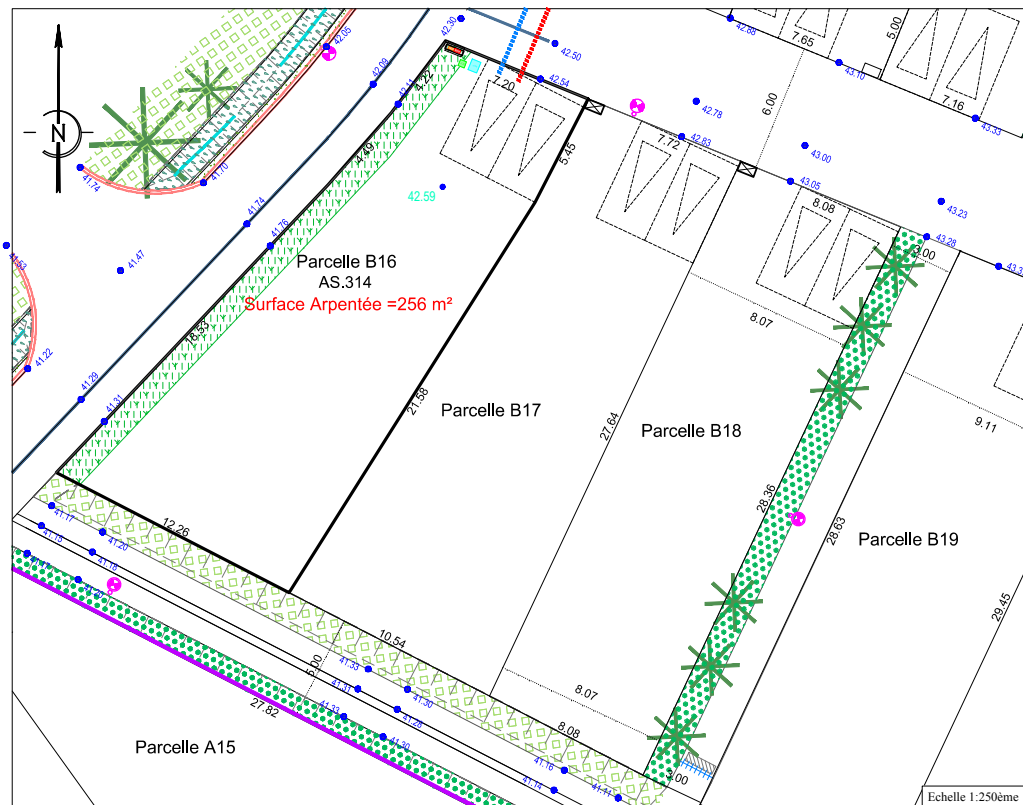

Légende

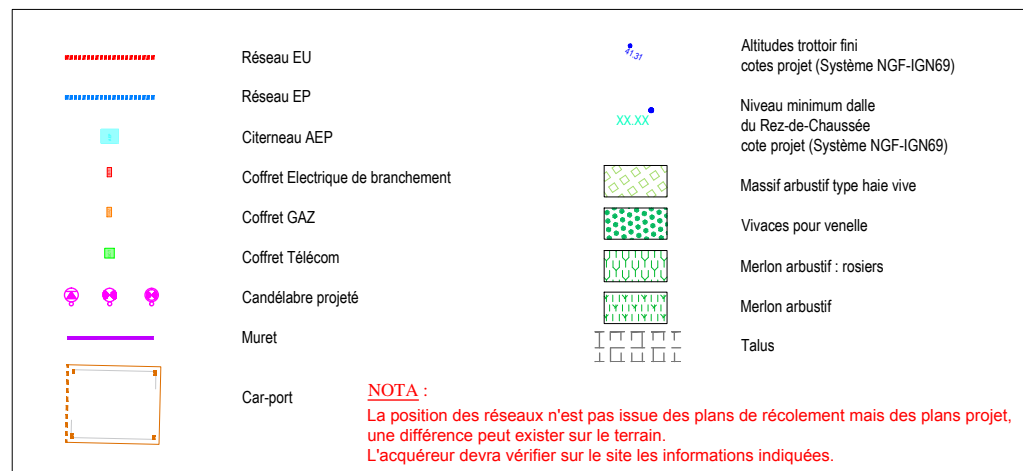

Parcelle B16

Référence cadastrale : Section AS

Surface arpentée : 256 m²


Numéro : 314

Plan de situation




Echelle 1:30 000ème

Plan d'ensemble

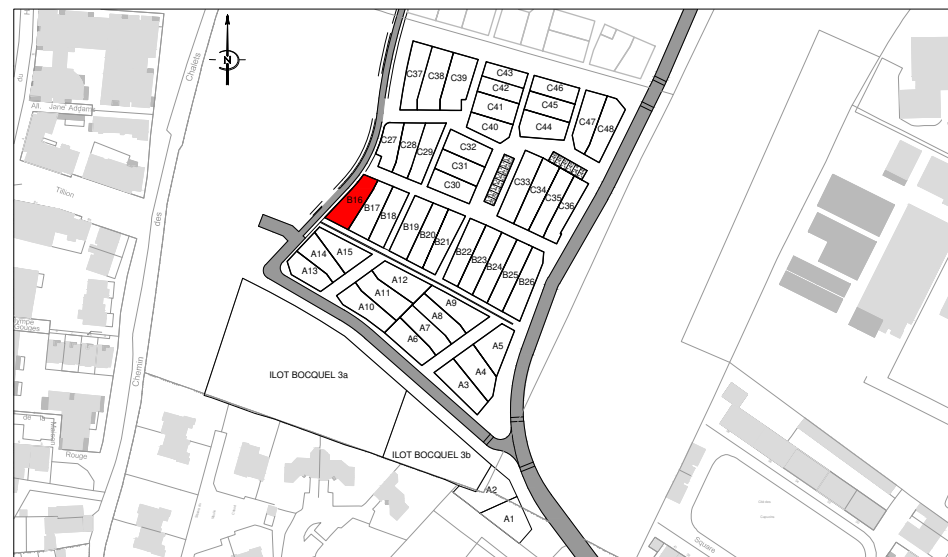


Echelle 1:2 500ème

Plan du Lot

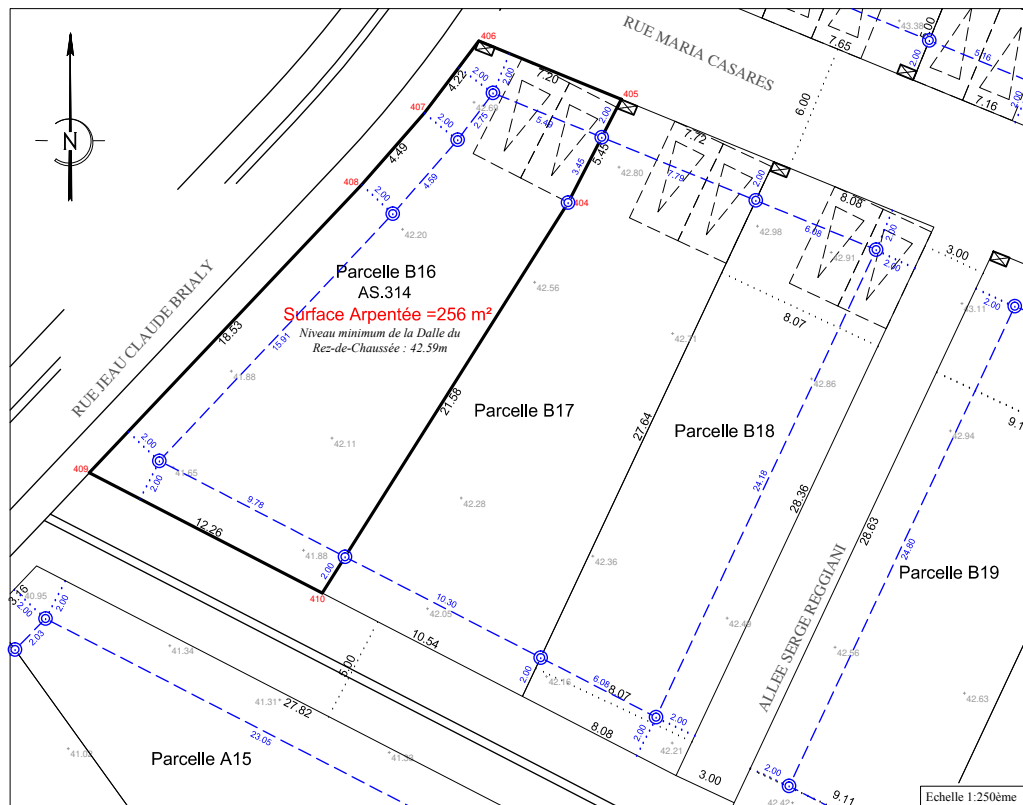


Légende

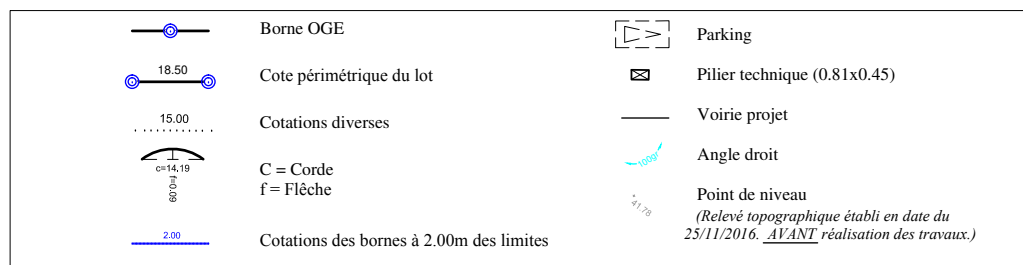


Coordonnées des Sommets			
SOMMET	X	Y	DISTANCE
404	1431920.26	6260498.87	5.45
405	1431922.75	6260503.71	7.20
406	1431916.09	6260506.44	4.22
407	1431913.54	6260503.07	4.49
408	1431910.59	6260499.70	18.53
409	1431897.86	6260486.23	12.26
410	1431908.76	6260480.61	21.58
404	1431920.26	6260498.87	
Superficie : 256 m²			

PLANIMETRIE : système RGF 93 - CC 47

Plan des Prescriptions

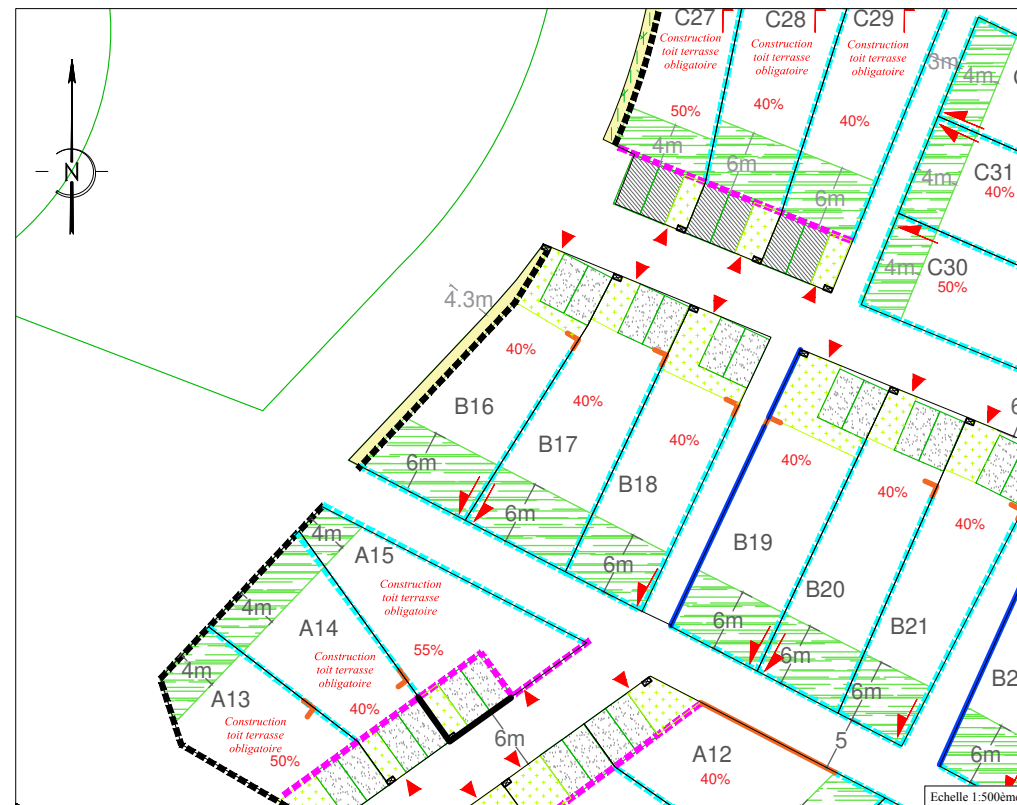

Légende

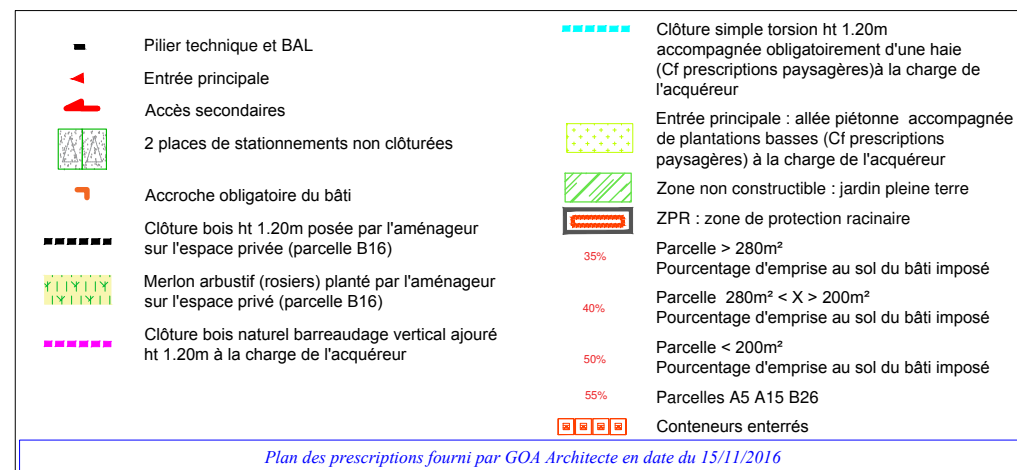

Plan des prescriptions fourni par GOA Architecte en date du 15/11/2016