



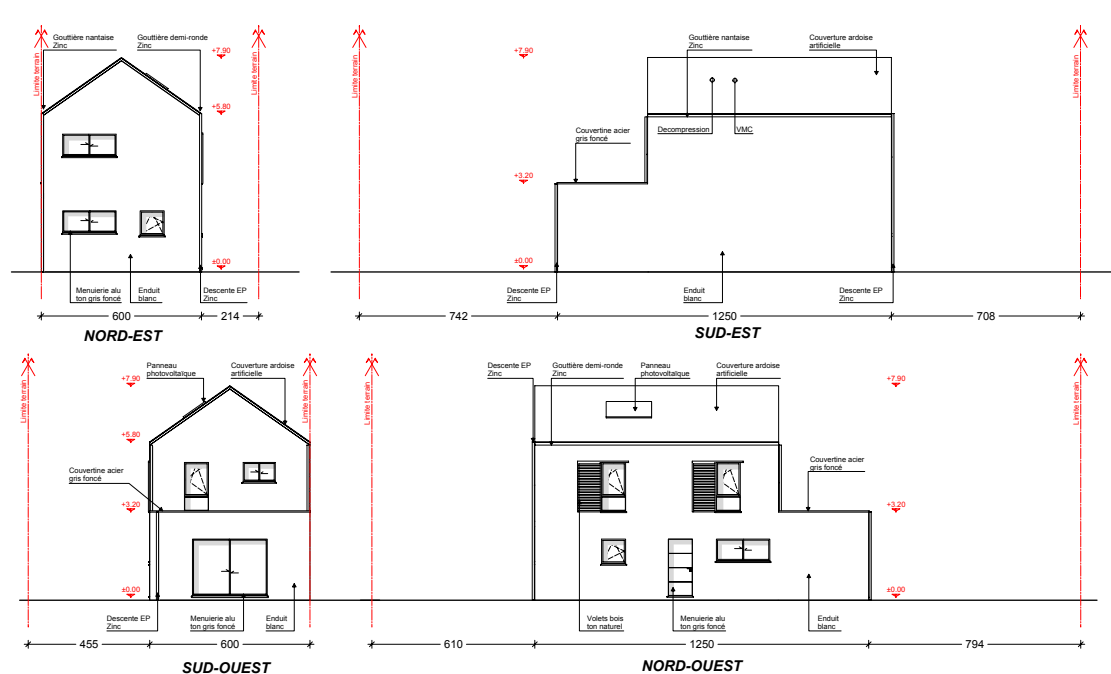


FACADES
Echelle : 1/50

Surface habitable	
RDC	
CELLIER	5.64 m²
CHAMBRE + S.E	13.25 m²
DGT	1.99 m²
PIECE DE VIE	36.31 m²
WC -01-	1.28 m²
	58.47 m²
Surface habitable	
R+1	
CHAMBRE -02-	10.58 m²
CHAMBRE -03-	10.19 m²
BUREAU	9.19 m²
DGT	2.88 m²
SDB	5.28 m²
WC -02-	1.61 m²
	39.73 m²


SURFACES
Total Shab : 98.21 m²
Total SDP : 100.96 m²
Emprise au sol : 75 m²

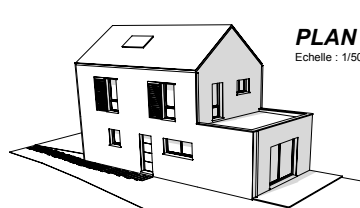


PLAN R+1
Echelle : 1/50

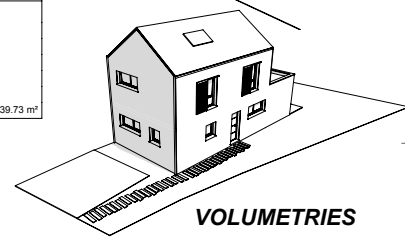


VOLUMETRIES

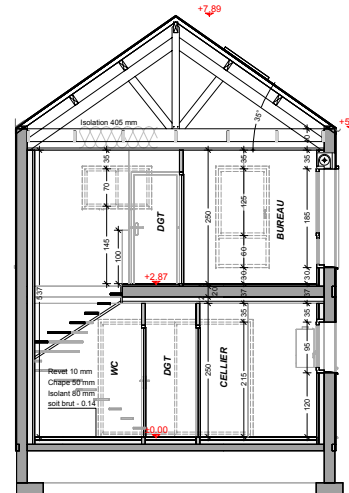



COUPE AA
Echelle : 1/50

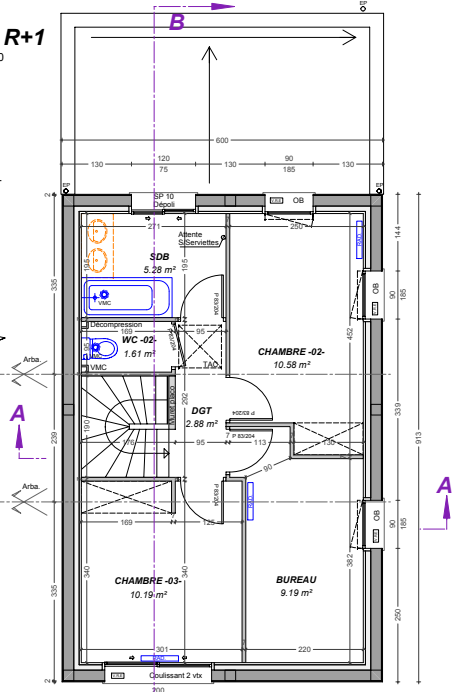


PLAN RDC
Echelle : 1/50

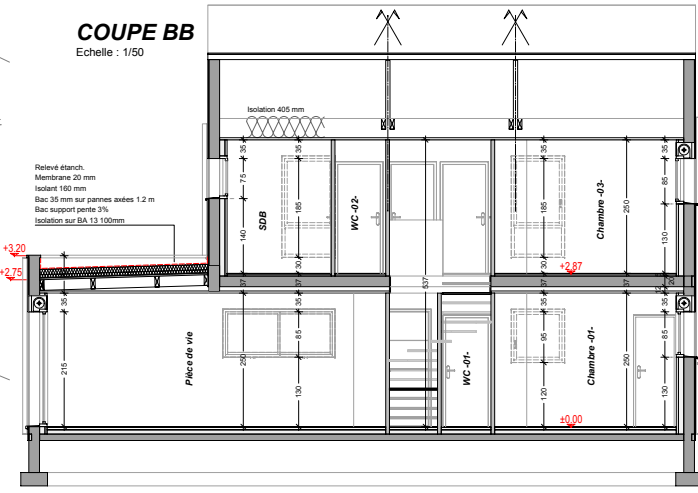

COUPE BB
Echelle : 1/50

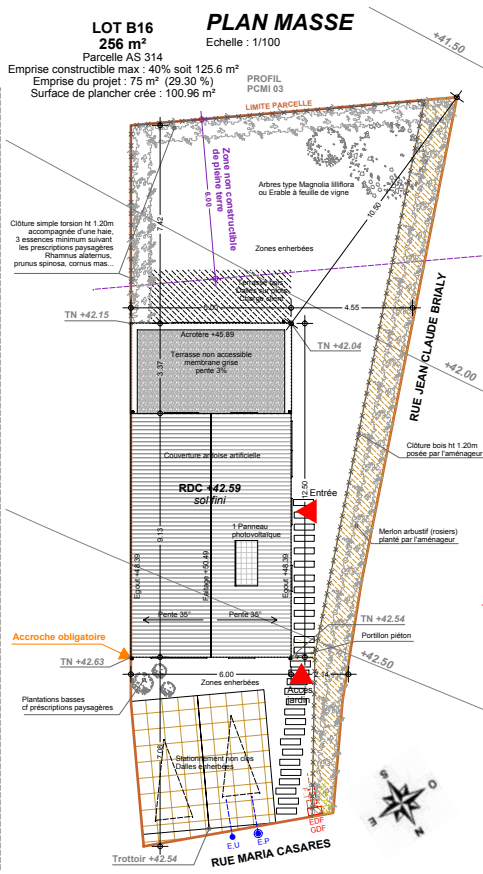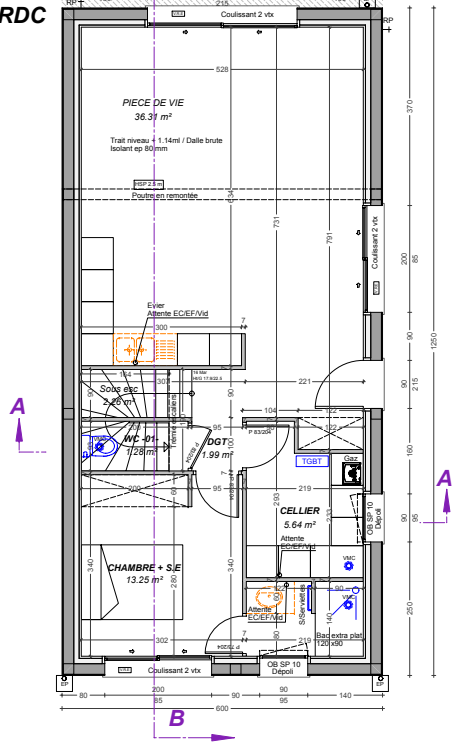

PLAN MASSE
Echelle : 1/100

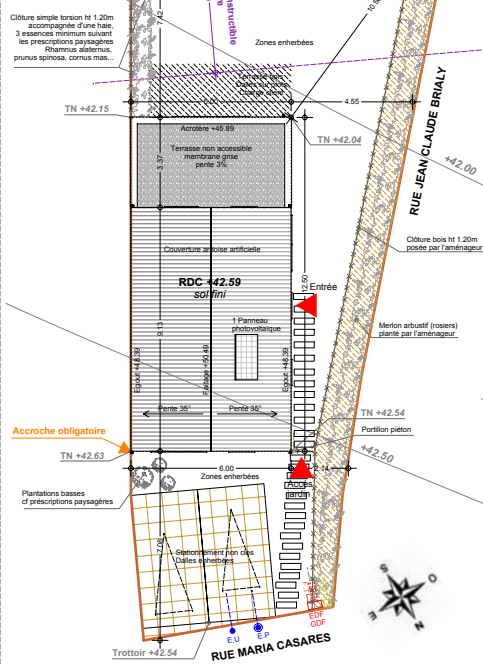

Accroche obligatoire

TN +42.63

Plantations basses de prescriptions paysagères

Zones enterrées

Detournement non des dalles existantes

6.00

Entrée

Trottoir +42.54

RUE MARIA CASARES

Logémaine

CONSTRUCTION D'UNE MAISON INDIVIDUELLE

Maitre d'Ouvrage

Mr Soulé, Mme Chevalier

Lieu de construction

ANGERS
ZAC des CAPUCINS
Ilot BOCQUEL
LOT B16

DOSSIER TECHNIQUE
PLANS - COUPES - FACADES
MAP CLIENT

Signature Maître d'Oeuvre // Signature Client // Date

Date d'édition :
30 AOUT 2017

Atelier
construction
& rénovation

